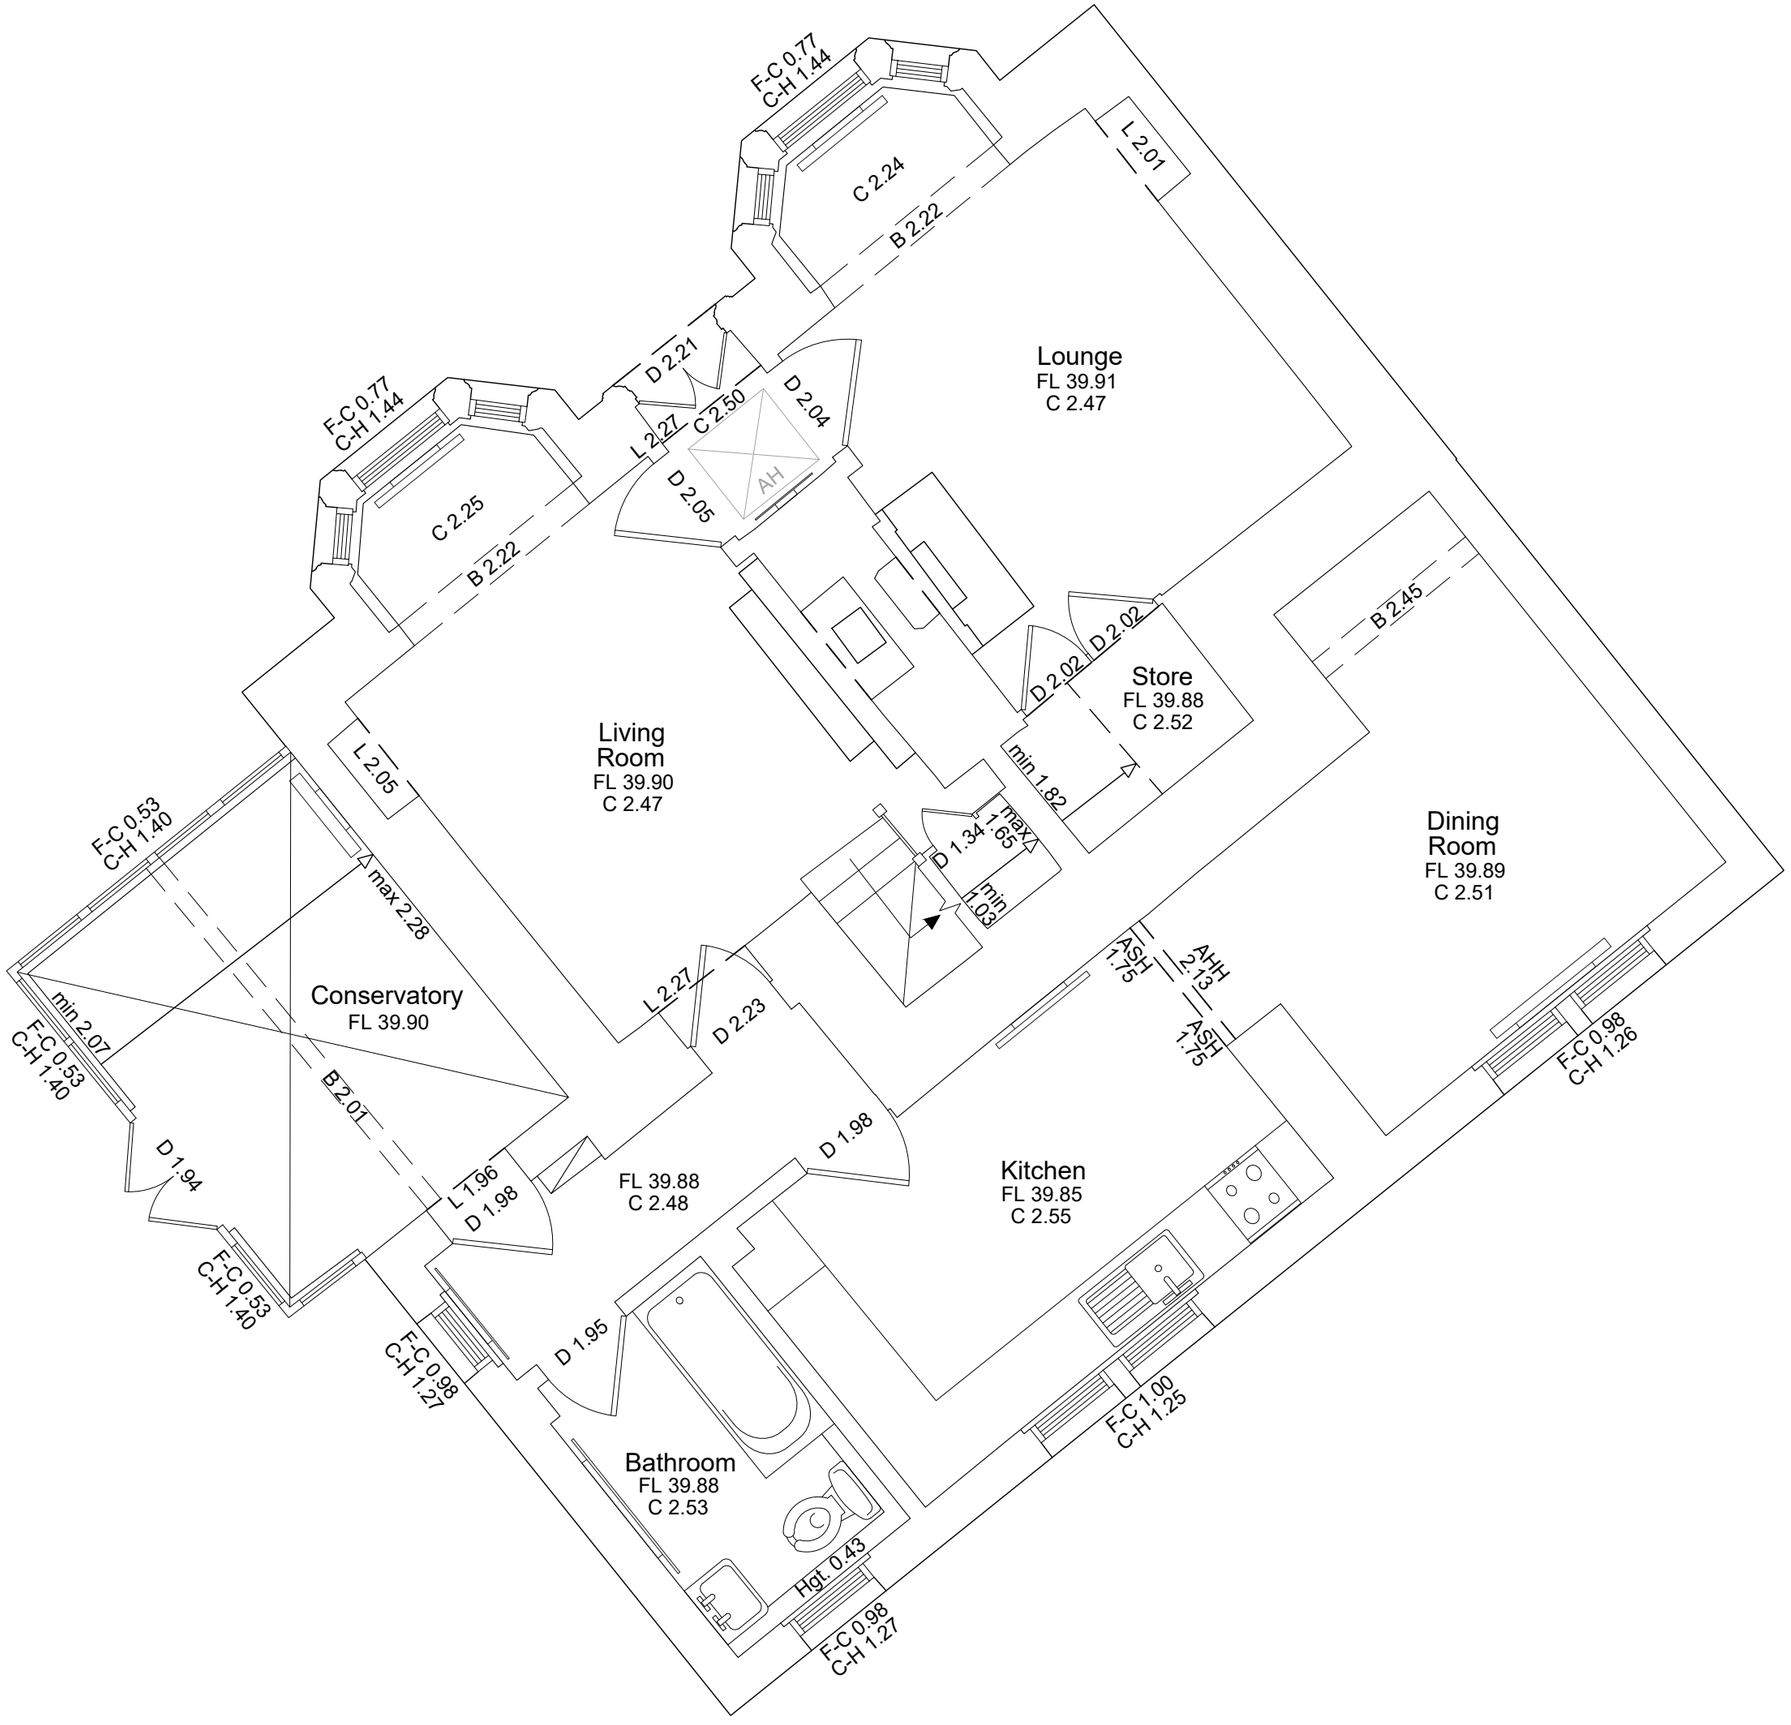


LEGEND

ACCESS HATCH	
AIR CONDITIONING	
A/C CONTROL PANEL	
ALARM SENSOR	AS
ARCH HEAD HEIGHT	AHH
ARCH SPRINGER HEIGHT	ASH
BEAM HEIGHT	B 1.23
BELL	
BLANKING PLATE	
BREAK GLASS	
CEILING	C 1.23
CEILING LIGHT	
CILL TO HEAD	C-H 1.23
CLOSE CIRCUIT CAMERA	CCTV
DISTRIBUTION BOARD	
DOOR HEAD HEIGHT	D 1.23
DOOR RELEASE	DR
DOUBLE SOCKET	
DUCTING	
EMERGENCY DOOR RELEASE	EDR
EMERGENCY EXIT LIGHTING	
EMERGENCY LIGHTING	
EXTRACTOR FAN	EF
FALSE / SUSPENDED CEILING	F 1.23
FAN	Fan
FIRE ALARM BELL	FA
FIRE EXTINGUISHER	FX
FLOOR TO CILL	F-C 1.23
FLUORESCENT LIGHTING	
FLOOR LEVEL	FL
FUSED SPUR	
HAND DRYER	HD
HOSE REEL	HR
HOT WATER BOILER	HWB
INSPECTION COVER	
LINTEL HEIGHT	L 1.23
LIGHT SWITCH / SINGLE	
LIGHT SWITCH / DOUBLE	
LIGHT SWITCH / TRIPLE	
LIGHT SWITCH / QUADRUPLE	
LOW VOLTAGE SUPPLY	LV
PHONE / DATA POINT	
PULL CORD SWITCH	
RADIATOR	
RAIN WATER PIPE	RWP
SINGLE SOCKET	
SKYLIGHT	
SLOPED CEILING	min 1.00 — max 2.00
SMOKE DETECTOR	SMD
SERVICE PIPE	SVP
SPOTLIGHT	
SWITCH	
SWITCHED FUSED SPUR	
THERMOSTAT	
UNKNOWN SERVICE	UN
WALL LIGHT	

Accuracy commensurate with scale of drawing.

N

SIGMA SURVEYS

PAVILION 2
BUCHANAN BUSINESS PARK
GLASGOW
G33 6HZ
Tel: 0141 779 7971
WWW.SIGMA-SURVEYS.COM

10 LOCHSIDE PLACE
EDINBURGH PARK
EDINBURGH
EH12 9RG
Tel: 0131 202 7861
DUDTES@SIGMA-SURVEYS.COM

SURVEYED	G. QUAIL	SCALE
DRAWN	G. QUAIL	1:50 (A3 Sheet)
CHECKED	J. ROMAN	

JAMES HUTCHISON GARDEN DESIGN

ARNGOMERY LODGE, KIPPEN

MEASURED BUILDING SURVEY
GROUND FLOOR

Job No.	Drawing No.	Date	Revision
24/030	24/030/02	March 2024	

REVISION	NOTES	DATE

Notes:

Grid relates to OS Active Network OSTN15.

All levels relate to OS Datum OSGM15.

THE SURVEY ASSOCIATION
Constructionline Silver Member
CHAS Accredited Contractor
Civil Aviation Authority
chartered ices
DroneSafe